




LEGENDE	
SYMBOLE	DESIGNATION
	Réserve de 100x100
	Réserve de 200x100
	Réserve de 400x200


LEGENDE	
SYMBOLE	DESIGNATION
	Réserve de 100x100
	Réserve de 200x100
	Réserve de 400x200

Réervations colonnes EDF/SG / FT
PH Bat A

Réervations colonnes EDF/SG / FT
PH Bat B

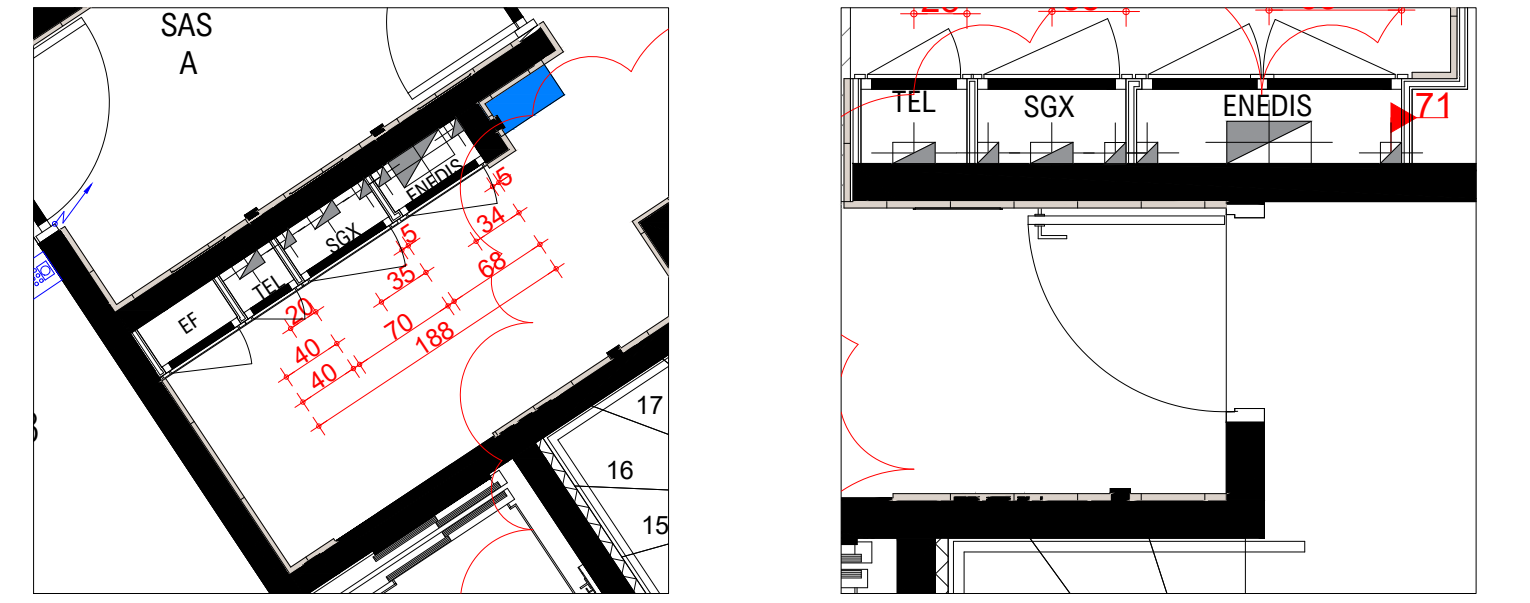

Réervations colonnes EDF/SG / FT
PH Bat C

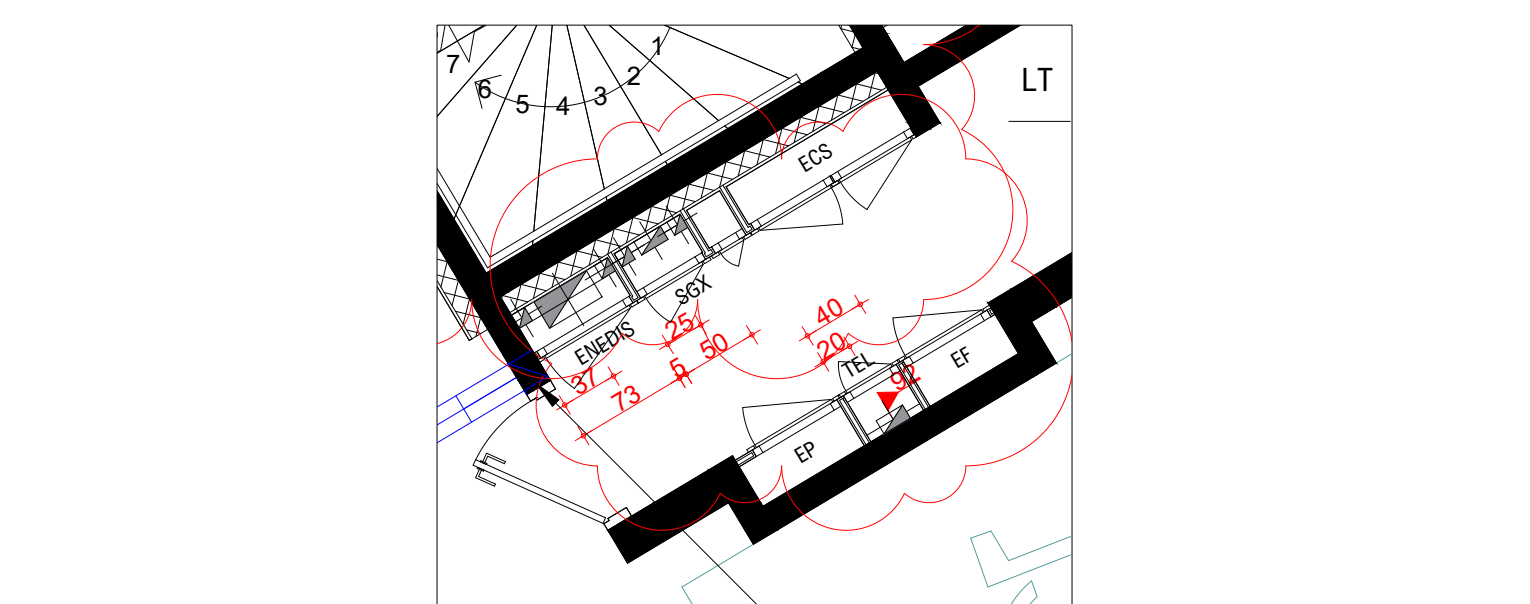

Archi/EDF
A-011 /001

Fond de plan :
Architecte → Dossier marche : 19.03.26
→ CVC : En attente des plans du lot CVC

Société Parisienne d'Equipeement Electrique
Siège social : 3bis rue Raymond Poincaré 93330 Neuilly sur Seine
Tel: 06 60 17 51 13
mail : sp2e93@hotmail.com - sp2e93.travaux@hotmail.com
SARL au capital de 7 500 € - SIRET 983 887 209 - RCS Bobigny



Projet de construction d'un ensemble immobilier de
60 logements et stationnement en rez-de-chaussée
82-90 rue de Paris
GONESSE - 95500

ENTREPRISE GENERALE
BOUYGUES BAT HABITAT SOCIAL
Agence PICARDIE
128 rue de Beauvais
60280 MARGNY LES COMPIEGNE

MAITRISE D'OEUVRE
ATELIERS 115 Architectes
115, Avenue Jean-Baptiste Clément
92100 Boulogne-Billancourt

MAITRISE D'OUVRAGE
LINKCITY
1, Avenue Eugène Freyssinet
78280 GUYANCOURT CEDEX

BUREAU D'ETUDE
ELITHIS - OTEIS
71 BIS Avenue Jean Jaurès BP 41249
21000 DIJON CEDEX
03 80 43 52 02

AFF: 043 ELECTRICITE 01

Plan d'implantation du RDC		
Ind.	MODIFICATIONS	Date
O	Première diffusion	03.04.26
A	Maj du plan archi reçu le 13.04.26	27.04.26
B	Maj du plan archi reçu le 25.06.26	29.06.26
C		
D		
E		
F		
Dessiné par : K.D. Vérifié par : I.A. Fait le : 27.03.26 Echelle : 1:100		
Ce document est la propriété SPE - il ne peut être ni reproduit, ni communiqué à des tiers sans l'autorisation écrite d'une personne mandatée spécialement.		

