
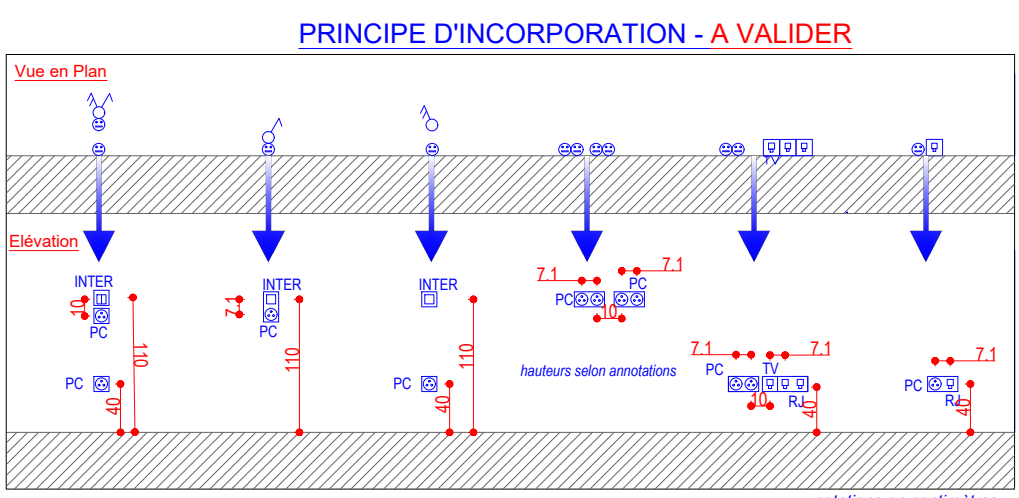


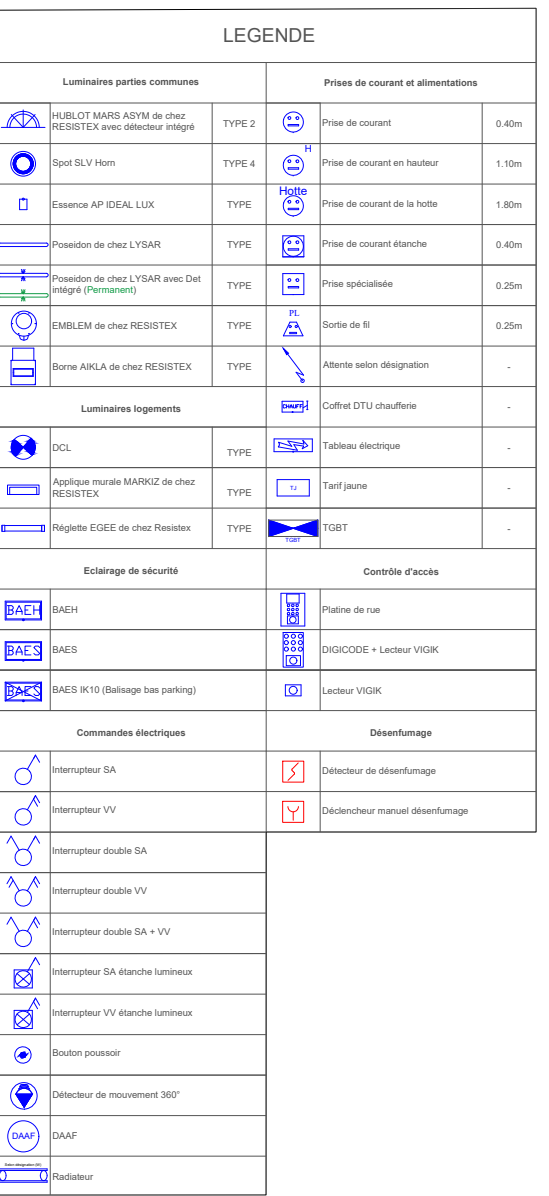

Archi/EDF  
**A-011 / 001**

**Fond de plan :**  
**Architecte → Dossier marche : 19.03.26**  
**→ CVC : En attente des plans du lot CVC**

**Société Parisienne d'Equipeement Electrique**  
Siège social : 3bis rue Raymond Poincaré 93330 Neuilly sur Marne  
Tel: 06 60 17 51 13

mail : [sp2e93@hotmail.com](mailto:sp2e93@hotmail.com) - [sp2e93.travaux@hotmail.com](mailto:sp2e93.travaux@hotmail.com)  
SARL au capital de 7 500 € - SIRET 983 887 209 - RCS Bobigny

**SE** Société  
Parisienne  
d'Équipement  
Électrique

Projet de construction d'un ensemble immobilier de  
60 logements et stationnement en rez-de-chaussée  
82-90 rue de Paris  
GONESSE - 95500

ENTREPRISE GENERALE

BOUYGUES BAT HABITAT SOCIAL  
Agence PICARDIE  
128 rue de Beauvais  
60280 MARGNY LES COMPIEGNE

**MAITRISE D'OEUVRE**  
**ATELIERS 115 Architectes**  
115, Avenue Jean-Baptiste Clément  
92100 Boulogne-Billancourt

**MAITRISE D'OUVRAGE**  
**LINKCITY**  
1, Avenue Eugène Freyssinet  
92820 GUYANCOURT CEDEX

BUREAU D'ETUDE

**ELITHIS - OTEIS**  
71 BIS Avenue Jean Jaurès BP 41249  
21000 DIJON CEDEX  
03 80 43 52 02

AFF: 043

ELECTRICITE

03

### Plan d'implantation du R+2

| Ind. | MODIFICATIONS                              | Date     |
|------|--------------------------------------------|----------|
| O    | Première diffusion                         | 07.05.26 |
| A    | Maj du fond de plan archi reçu le 13.05.26 | 16.05.26 |
| B    | Maj du plan archi reçu le 25.06.26         | 29.06.26 |
| C    |                                            |          |
| D    |                                            |          |
| E    |                                            |          |
| F    |                                            |          |

|   |     |               |     |           |          |           |       |
|---|-----|---------------|-----|-----------|----------|-----------|-------|
| Dessiné par :   | K.D | Vérifié par : | I.A | Fait le : | 27.03.26 | Echelle : | 1:100 |
| Ce document est la propriété SP2E - Il ne peut être ni reproduit, ni communiqué à des tiers sans l'autorisation écrite d'une personne mandatée spécialement |     |               |     |           |          |           |       |